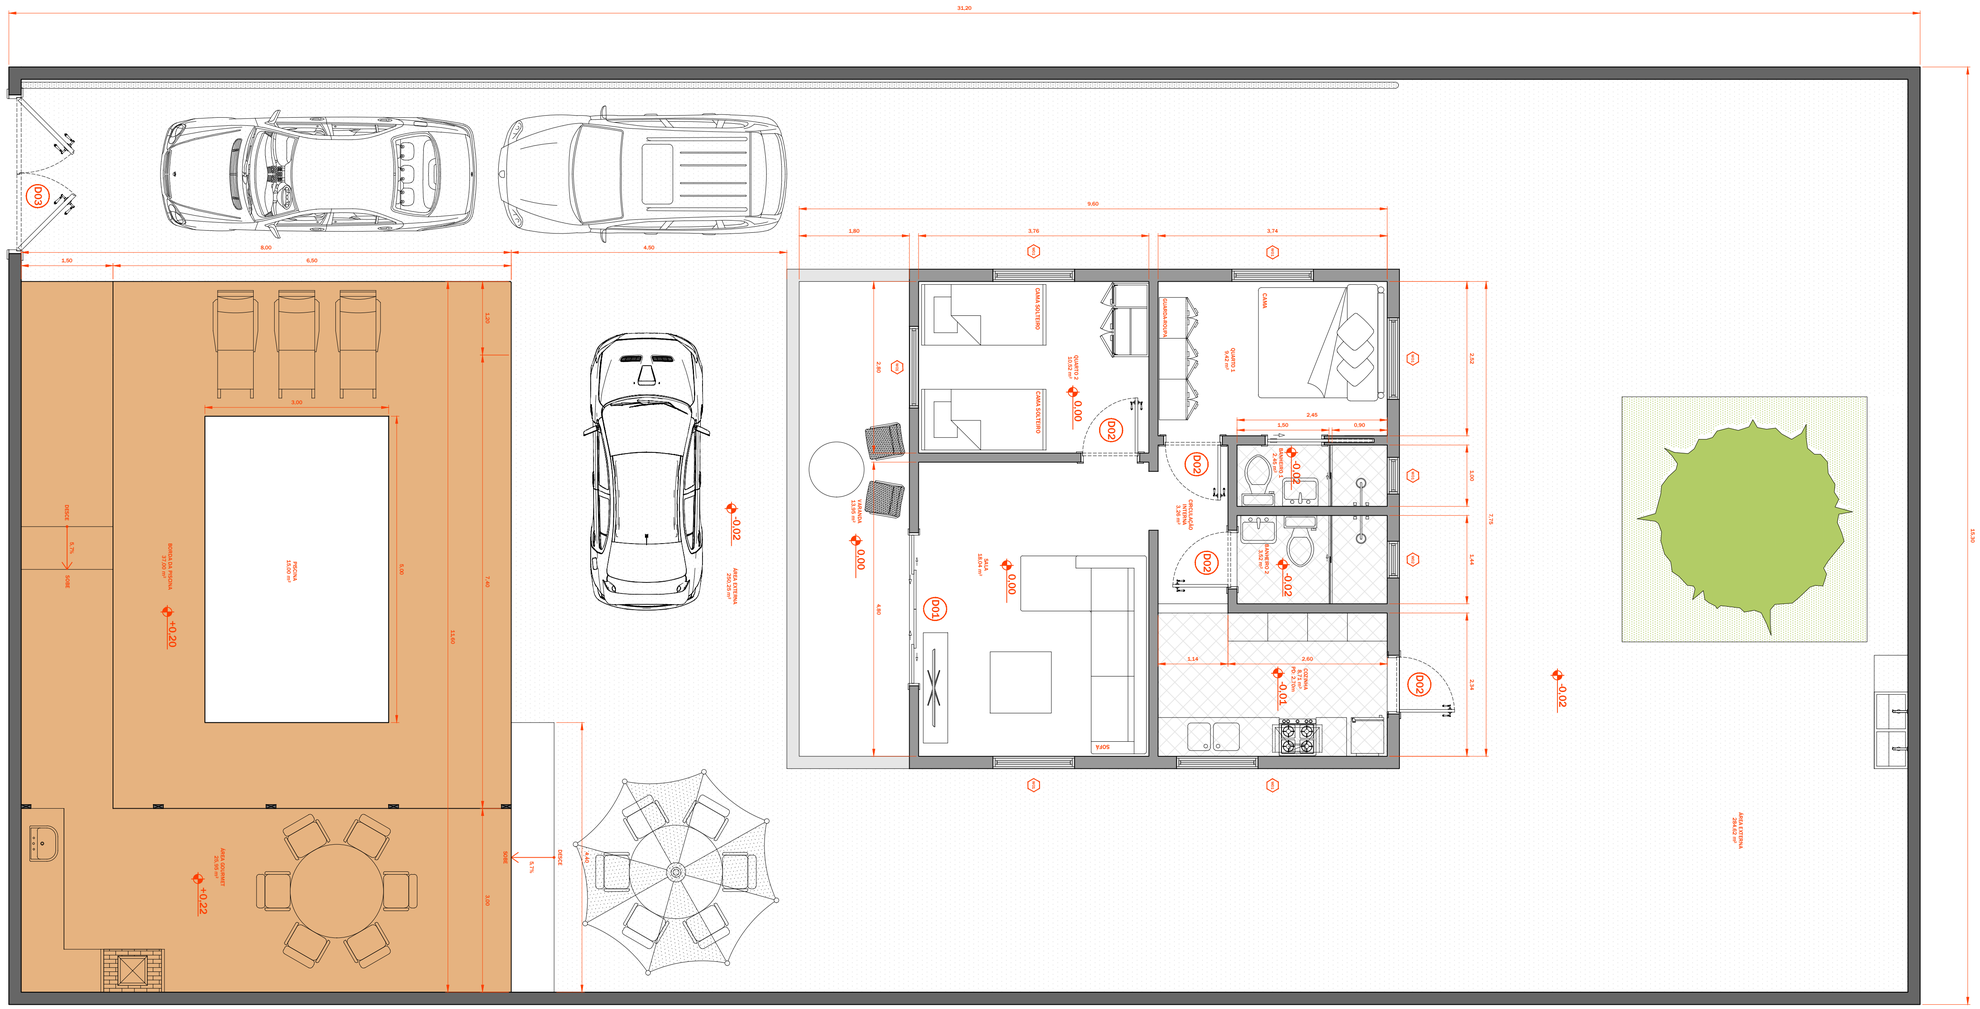

1 PLANTA BAIXA

ESCALA: 1:50

W01	W02	D01	D02
Janela: 1,33 x 1,26 x 0,15	Janela: 0,60 x 0,60 x 0,15	Porta: 2,42 x 2,10 x 0,15	Porta: 0,90 x 2,10 x 0,15

0 5 10

ENG. PEDRO AUGUS

ILHA DO GOV ERNADOR

© 2023

N

PROJETO

CASA DE PRAIA

LOCALIZAÇÃO: R. Pureza - Balneário São Pedro II, 18

DATA: 01/03/2023 DATA

PROJETO Nº: 2023.02 Nº

REVISÃO	DATA
1	
2	
3	
4	
5	
6	

NOTAS:

1. TODAS AS DIMENSÕES COTADAS NÃO CONSIDERAM A ESPESSURA FINAL DAS PAREDES EXCETO SE ESCRITO O OPOSTO.
2. TODAS AS DIMENSÕES ESTÃO EM METROS, EXCETO SE ESCRITO O OPOSTO

3. UTILIZAR PEDRA SÃO TOMÉ OU PISO ATÉRMICO COMO REVESTIMENTO PARA A BORDA DA PISCINA

4. O REVESTIMENTO DA ÁREA EXTERNA DEVE SER CONCRETO ESTAMPADO, CONCRETO QUEIMADO OU CHAPAS CIMENTÍCIAS

5. PREVER DESNÍVEL PARA ESCOAMENTO DE ÁGUA DA CHUVA E LIMPEZAS ÚMIDAS

TÉRREO

PLANTA BAIXA

ESCALA: 1:50

A1.2

PROJETISTA: PEDRO AUGUSTO