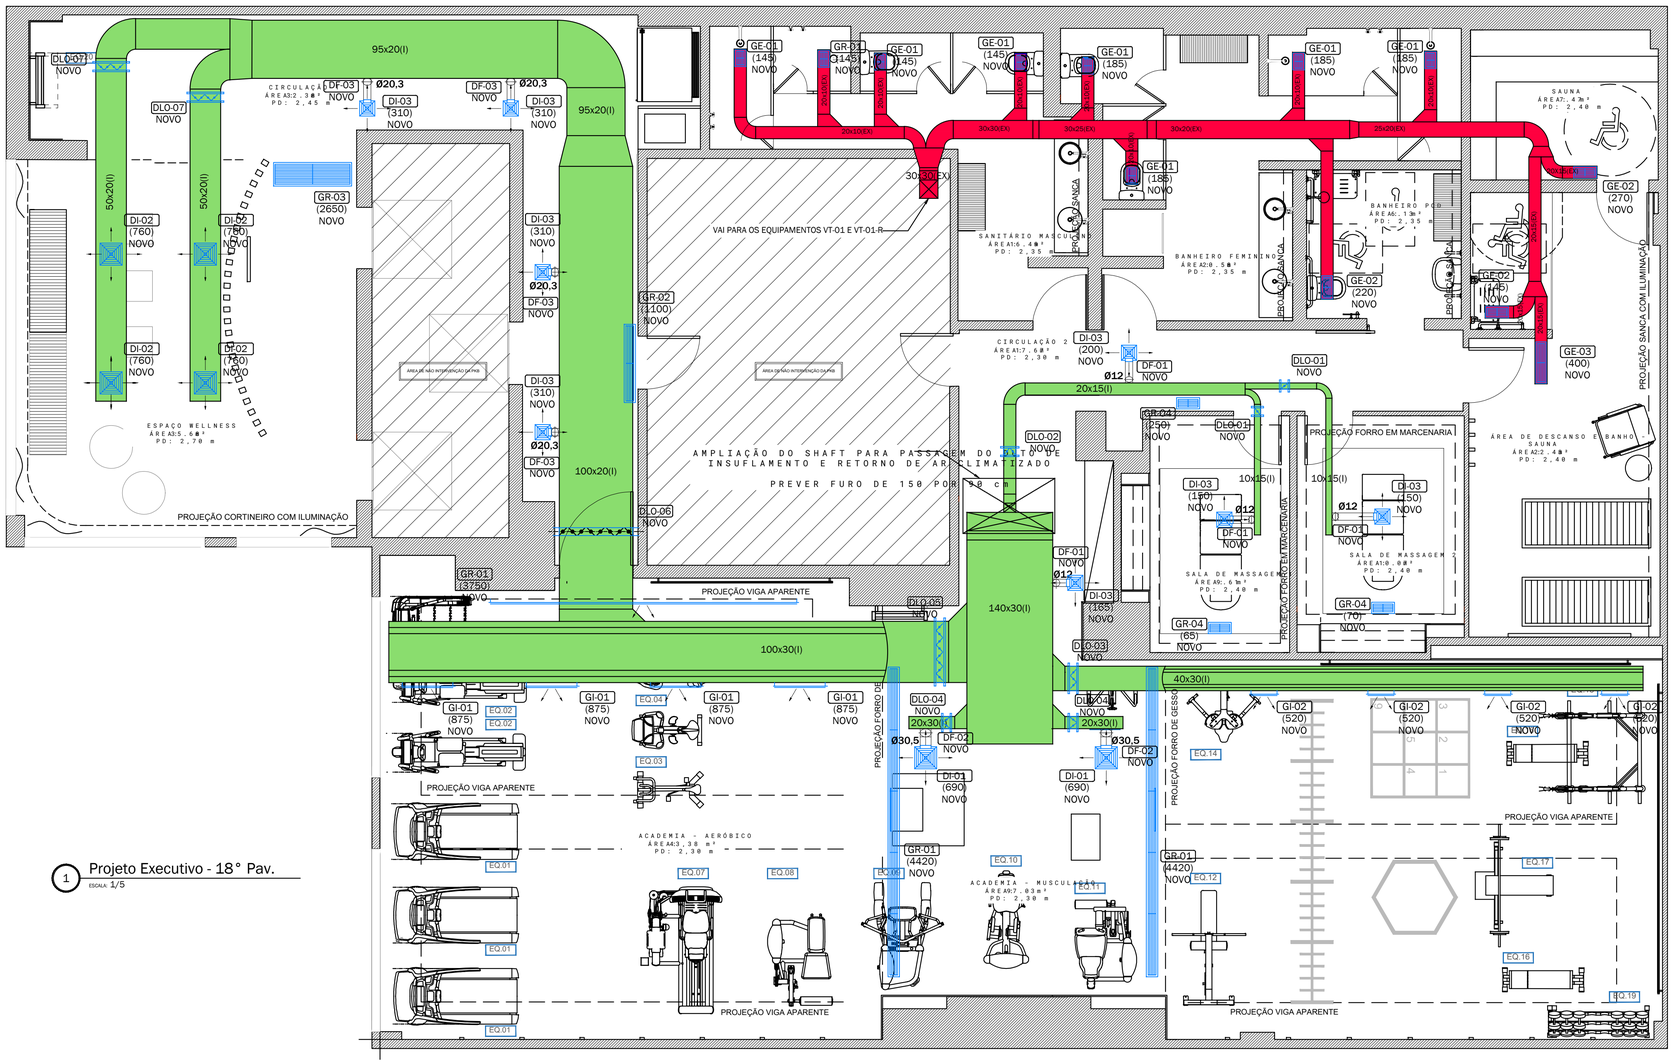

1 Projeto Executivo - 18° Pav.
ESCALA 1/5

0 5 10

LEGENDA DE REPRESENTAÇÃO GRÁFICA - VENTILAÇÃO MECÂNICA

- NOVA TUBULAÇÃO A SER EXECUTADA DE RETORNO DE ÁGUA GELADA (RAG) PARA PRESSÃO DE TRABALHO DE 300 PSI.
- NOVA TUBULAÇÃO A SER EXECUTADA DE RETORNO DE ÁGUA GELADA (RAG) PARA PRESSÃO DE TRABALHO DE 300 PSI.
- PONTO DE DRENO
- PONTO DE FORÇA
- PONTO DE COLETA DE ESGOTO PARA COIFA OU RALO SIFONADO
- QUADRO ELETRICO DOS EQUIPAMENTOS
- PONTO DE ÁGUA PARA MANUTENÇÃO DO EQUIPAMENTO
- TUBULAÇÃO FRIGORÍGENA / TUBULAÇÃO DE ÁGUA GELADA
- TUBULAÇÃO COM PROTEÇÃO CONTRA INTEMPÉRIES
- DUTO DE INSULFAMENTO EM CHAPA DE AÇO GALVANIZADO COM ISOLAMENTO TÉRMICO.
- DUTO DE RETORNO EM CHAPA DE AÇO GALVANIZADO COM ISOLAMENTO TÉRMICO.
- DUTO DE EXAUSTÃO EM CHAPA DE AÇO GALVANIZADO SEM ISOLAMENTO TÉRMICO.
- DUTO DE AR EXTERNO EM CHAPA DE AÇO GALVANIZADO SEM ISOLAMENTO TÉRMICO.
- DUTO DE INSUFLAMENTO GIROVAL NA COR A SER DEFINIDA PELA ARQUITETURA
- DUTO FLEXIVEL COM REGISTRO
- DUTO EXISTENTE A MANTER
- DUTO A REMOVER (HACHURA PADRÃO ANSI 31)
- PONTO DE DRENO PARA FANCOIL
- EQUIPAMENTOS NOVOS A INSTALAR
- EQUIPAMENTOS EXISTENTES A MANTER (POSSUI INDICAÇÃO ABAIXO DO LABEL)
- EQUIPAMENTOS EXISTENTES A REMOVER (POSSUI INDICAÇÃO ABAIXO DO LABEL)
- EQUIPAMENTOS EXISTENTES A REMANEJAR (POSSUI INDICAÇÃO ABAIXO DO LABEL)
- ALÇAPÃO DE ACESSO
- VÁLVULA ESFERA PARA PRESSÃO DE TRABALHO DE 250 PSI.
- VÁLVULA BALANCEADORA PARA PRESSÃO DE TRABALHO DE 250 PSI.
- SEPTO ESTANQUE
- TERMOSTATO
- DERIVADOR "Y"(BRANCH)
- TOMADA DE AR EXTERIOR
- EXAUSTÃO
- INSUFLAMENTO
- DAMPER DE LÂMINAS OPOSTAS
- DAMPER DE SOBREPRESSÃO
- (####) VAZÃO EM m³/h
- (I) INSUFLAMENTO
- (R) RETORNO
- (EX) EXAUSTÃO
- (AE) AR EXTERIOR
- (DI) DIFUSOR DE INSUFLAMENTO
- (DP) DIFUSOR DE PISO
- (GI) GRELHA DE INSUFLAMENTO
- (GR) GRELHA DE RETORNO
- (GE) GRELHA DE EXAUSTÃO
- (DLO) DAMPER DE LÂMINAS OPOSTAS
- (DFX) DUTO FLEXÍVEL
- (TAE) TOMADA DE AR EXTERIOR

ZZ-YYY
- FC: FANCOL
- SC: SELF CONTAINED
- UE: UNIDADE EVAPORADORA
- UC: UNIDADE CONDENSADORA
- VE: VENTILADOR
- NÚMERO
- AR CONDICIONADO

NOTAS GERAIS

1. CONSULTAR OS DESENHOS DE DETALHES TÍPICOS, PARA COTAÇÃO E EXECUÇÃO DA OBRA PARA DEFINIÇÃO COMPLETA DO ESCOPO DE SERVIÇOS DO INSTALADOR DEVERÁ AINDA CHECAR OS ESPAÇOS PREVISTOS, COM INTUITO DE PROPOR EQUIPAMENTOS E/OU MATERIAIS COM DIMENSÕES FÍSICAS COMPATÍVEIS COM OS RESPECTIVOS LOCAIS PREVISTOS PARA INSTALAÇÃO DOS MESMOS;
2. ANTES DO INÍCIO DA OBRA, A EMPRESA RESPONSÁVEL PELA EXECUÇÃO DEVERÁ REALIZAR UM LEVANTAMENTO NO LOCAL, VERIFICANDO AS INFORMAÇÕES APRESENTADAS NO PROJETO E INTERFERÊNCIAS NA OBRA. QUALQUER ALTERAÇÃO QUE SE FAÇA NECESSÁRIO NA EXECUÇÃO DA OBRA A GERENCIADORA DEVERÁ SER COMUNICADA ANTES DA EXECUÇÃO DO SERVIÇOS, E A INSTALADORA DEVERÁ ENTREGAR AS-BUILT NO TÉRMINO DA OBRA;
3. DIMENSÕES EM CENTIMETRO, EXCETO QUANDO INDICADO DE OUTRA FORMA;
4. TODOS OS FUROS PARA PASSAGEM DE DUTOS, TUBULAÇÕES E/OU ELETRODUTOS, DEVERÃO SER A INSTALAÇÃO DOS MESMOS;
5. CONFERIR MEDIDAS NO LOCAL;
6. PROJETO DESENVOLVIDO SEGUNDO ORIENTAÇÕES DA ABNT 16401-1/3 E ANVISA RE#9;
7. EFETUAR AS DEVIDAS ADEQUAÇÕES E RECOPOSIÇÕES DE ALVENARIA/FORRO. (FUROS, CONSTRUÇÃO DE PAREDES, ETC.);
8. A RETIRADA DE MATERIAIS OU EQUIPAMENTOS INUSITADOS DEVERÁ SER REALIZADA POR CONTA DO INSTALADOR;
9. O INSTALADOR DEVERÁ FORNECER LAUDO DE TESTES, GARANTIA DOS EQUIPAMENTOS E DA OBRA E ART NA CONCLUSÃO DA OBRA;
10. O INSTALADOR DEVERÁ VERIFICAR A TENSÃO ELÉTRICA DO LOCAL ANTES DA COMPRA DOS EQUIPAMENTOS DE FORMA FORNECER O EQUIPAMENTO CONFORME A TENSÃO DE OPERAÇÃO DA AGÊNCIA;
11. CONSULTAR PROJETO ELÉTRICO PARA O ALIMENTADOR DOS EQUIPAMENTOS;
12. VERBA DE ADEQUAÇÕES PARA COMPATIBILIZAÇÃO DE ELEMENTOS DE DIFUSÃO, DUTOS E EQUIPAMENTOS COM AS DEMAIS DISCIPLINAS NA OBRA.
13. NOTAS REFERENTES AO SISTEMA SPLIT SYSTEM:
   - 13.1. AS TUBULAÇÕES DE GÁS REFRIGERANTE DEVERÃO SER DIMENSIONADAS CONFORME ESPECIFICAÇÕES DO FABRICANTE E ISOLADAS TERMICAMENTE COM ESPUMA ELASTOMÉRICA DE ESTRUTURA CELULAR FECHADA. AS LINHAS DE SUCÇÃO E LÍQUIDO, DEVERÃO POSSUIR UMA ESPUMA PARA CADA, NAS DIMENSÕES CONFORME BITOLA DAS MESMAS;
   - 13.2. 13.2. A DISTÂNCIA ENTRA A UNIDADE CONDENSADORA E EVAPORADORA NÃO DEVERÁ ULTRAPASSAR O RECOMENDADO NO MANUAL DO INSTALAÇÃO DO EQUIPAMENTO. PARA EVENTUAL INSTALAÇÃO COM LINHA ACIMA DO PADRÃO ESPECIFICADO PELO FABRICANTE, DEVERÁ SER ADOTADO AS DIMENSÕES E INSTALAÇÃO DE ACESSÓRIOS CONFORME ESPECIFICAÇÃO DE LINHAS LONGAS DO FABRICANTE DO EQUIPAMENTO, OBEDECENDO ACS LIMITES DETERMINADOS NO MANUAL DE INSTALAÇÃO;
   - 13.3. DEVERÁ SER ANALISADO PELA INSTALADORA A MELHOR MANEIRA PARA EXECUÇÃO DAS TUBULAÇÕES. O INSTALADOR PODERÁ MODIFICAR O ENCAMINHAMENTO DA TUBULAÇÃO DE COBRE, PARA CONRURIR SEU TRAJETO OU DESVIAR DE EVENTUAIS INTERFERÊNCIAS, DESDE QUE SEJAM RESPEITADOS OS LIMITES IMPOSTOS PELO FABRICANTE DOS EQUIPAMENTOS;
   - 13.4. A INTERLIGAÇÃO ENTRE A UNIDADE CONDENSADORA E A UNIDADE EVAPORADORA DEVERÁ SER REALIZADA ATRAVÉS DE TUBULAÇÕES DE COBRE. AS TUBULAÇÕES QUE INTERLIGAM A UNIDADE EVAPORADORA (AFUCÇÃO PARA SISTEMA DE MINI SPLIT DE AMBIENTE);
   - 13.5. O INSTALADOR DE SISTEMA DE AR CONDICIONADO DEVERÁ FORNECER E INSTALAR AS FIAÇÕES E ELETRODUTOS DOS TERMOSTATOS ATÉ AS RESPECTIVAS UNIDADES CONDICIONADORAS;
   - 13.6. PARA LOCAIS INTERNOS OU EMBUTIDOS EM ALVENARIA, PREVER ENVOLVIMENTO NAS TUBULAÇÕES DE GÁS REFRIGERANTE E INTERLIGAÇÕES ELÉTRICAS COM FITA PVC;
   - 13.7. PREVER INTERLIGAÇÃO ENTRE O DRENO DA UNIDADE EVAPORADORA A A REDE DE DRENAGEM A SER EXECUTADA. A TUBULAÇÃO DOS DRENOS DEVERÁ SER EM DE PVC SOLDÁVEL DE NO MÍNIMO Ø20mm E ISOLADA TERMICAMENTE COM ESPUMA DE POLIETILENO EXPANDIDO. A TUBULAÇÃO DEVERÁ SER EMBUTIDA NAS PAREDES E ENCAMINHADAS PARA REDE DE PLUVIAL. PREVER SIFÃO E INCLINAÇÃO MÍNIMA DE 2% NA TUBULAÇÃO DE DRENO. PARA EQUIPAMENTOS TIPO CASSETE E DE EMBUTIR NO FORRO (BUILT-IN) CASO NÃO SEJA POSSÍVEL A DEVIDA INCLINAÇÃO, PODERÃO SER UTILIZADAS AS BOMBAS DE DRENO FORNECIDAS PELO FABRICANTE DO EQUIPAMENTO
   - 13.8. OS EQUIPAMENTOS DEVERÃO POSSUIR ETIQUETA COM IDENTIFICAÇÃO, CONFORME ESPECIFICAÇÕES DO PROJETO, INCLUINDO O TAG, CAPACIDADE TÉRMICA, PRESSÃO ESTÁTICA TOTAL, CLASSE DOS FILTROS, TENSÃO DE OPERAÇÃO, CONSUMO ELÉTRICO E A DATA DE INSTALAÇÃO;
   - 13.9. AS CONDENSADORAS DEVERÃO FICAR AFASTADAS DA PAREDE NO MÍNIMO 20cm;
   - 13.10. AS UNIDADES CONDENSADORAS DEVERÃO SER INSTALADAS SOBRE CALÇOS DE NEOPRENE DE 2,5 cm DE ALTURA;
14. NOTAS REFERENTES AO SISTEMA DE DISTRIBUIÇÃO DE AR E EQUIPAMENTOS PARA EMBUTIR DUTOS:
   - 14.1. TODOS OS DUTOS DEVERÃO SER EM CHAPA DE AÇO GALVANIZADO DO TIPO TDC OU GIROVAL CONSTRUÍDOS NAS SEÇÕES RECOMENDADAS PELA ABNT NBR 16401 E NOS MÉTODOS RECOMENDADOS PELA SMACNA;
   - 14.2. O INSTALADOR DEVERÁ FORNECER E INSTALAR OS VENTILADORES, VENEZIANAS, GRELHAS E DUTOS PARA EXAUSTÃO E VENTILAÇÃO MECÂNICA;
   - 14.3. PREVER JANELA DE INSPEÇÃO PARA LIMPEZA DOS DUTOS A CADA 3M;
   - 14.4. TODAS AS CURVAS E JOELHOS DEVERÃO TER VIDOS DIRECIONAIS CONFORME NORMA ASHRAE;
   - 14.5. O INSTALADOR DEVERÁ FAZER TODO O BALANCEAMENTO DAS VAZÕES DE INSUFLAMENTO E DE AR EXTERIOR / EXAUSTÃO CONFORME INDICADO NO PROJETO;
   - 14.6. PREVER ALÇAPÃO NO FORRO FALSO PARA ACESSO A MANUTENÇÃO DE VENTILADORES, DAMPERS E JANELAS DE INSPEÇÃO DOS DUTOS

LISTA DE ITENS - NOVOS

TAG	DESCRIÇÃO	ESPECIFICAÇÃO	QUANTIDADE
DI-01	DIFUSOR DE 4 VIAS COM CAIXA PLENUM	DIFUSOR QUADRADO DE 4 VIAS COM REGISTRO E CAIXA PLENUM	2 Unidades
		Marca de referência: Trox; Modelo: ADLQ-AK-AG; TAM.: 4; 412x313 mm	
DI-02	DIFUSOR DE 4 VIAS SEM CAIXA PLENUM	DIFUSOR QUADRADO DE 4 VIAS COM REGISTRO	4 Unidades
		Marca de referência: Trox; Modelo: ADLQ-AG; TAM.: 4; 412x360 mm	
DI-03	DIFUSOR DE 4 VIAS COM CAIXA PLENUM	DIFUSOR QUADRADO DE 4 VIAS COM REGISTRO E CAIXA PLENUM	8 Unidades
		Marca de referência: Trox; Modelo: ADLQ-AK-AG; TAM.: 2; 300x255 mm	
GI-01	GRELHA DE DUPLA DEFLEXÃO - INSUFLAÇÃO	GRELHA DE DUPLA DEFLEXÃO COM REGISTRO	4 Unidades
		Marca de referência: Trox; Modelo: AT-AG; 825x125 mm	
GI-02	GRELHA DE DUPLA DEFLEXÃO - INSUFLAÇÃO	GRELHA DE DUPLA DEFLEXÃO COM REGISTRO	4 Unidades
		Marca de referência: Trox; Modelo: AT-AG; 425x125 mm	
DLO-01	DAMPER DE LÂMINAS OPOSTAS COM REGULAGEM MANUAL	DAMPER DE REGULAGEM MANUAL	2 Unidades
		Marca de referência: Trox; Modelo: RL-B; 100x150 mm	
DLO-02	DAMPER DE LÂMINAS OPOSTAS COM REGULAGEM MANUAL	DAMPER DE REGULAGEM MANUAL	1 Unidades
		Marca de referência: Trox; Modelo: RL-B; 200x150 mm	
DLO-03	DAMPER DE LÂMINAS OPOSTAS COM REGULAGEM MANUAL	DAMPER DE REGULAGEM MANUAL	1 Unidades
		Marca de referência: Trox; Modelo: RL-B; 400x300 mm	
DLO-04	DAMPER DE LÂMINAS OPOSTAS COM REGULAGEM MANUAL	DAMPER DE REGULAGEM MANUAL	2 Unidades
		Marca de referência: Trox; Modelo: RL-B; 200x300 mm	
DLO-05	DAMPER DE LÂMINAS OPOSTAS COM REGULAGEM MANUAL	DAMPER DE REGULAGEM MANUAL	1 Unidades
		Marca de referência: Trox; Modelo: RL-B; 1000x300 mm	
DLO-06	DAMPER DE LÂMINAS OPOSTAS COM REGULAGEM MANUAL	DAMPER DE REGULAGEM MANUAL	1 Unidades
		Marca de referência: Trox; Modelo: RL-B; 1000x200 mm	
DLO-07	DAMPER DE LÂMINAS OPOSTAS COM REGULAGEM MANUAL	DAMPER DE REGULAGEM MANUAL	2 Unidades
		Marca de referência: Trox; Modelo: RL-B; 500x200 mm	
GR-01	GRELHA DE ALETAS FIXAS - RETORNO	GRELHA DE ALETAS FIXAS COM REGISTRO	3 Unidades
		Marca de referência: Trox; Modelo: AH; 5000x125 mm	
GR-02	GRELHA DE ALETAS FIXAS - RETORNO	GRELHA DE ALETAS FIXAS COM REGISTRO	1 Unidades
		Marca de referência: Trox; Modelo: VAT-AG; 1225x125 mm	
GR-03	GRELHA DE ALETAS FIXAS - RETORNO	GRELHA DE ALETAS FIXAS COM REGISTRO	1 Unidades
		Marca de referência: Trox; Modelo: VAT-AG; 1225x325 mm	
GR-04	GRELHA DE ALETAS FIXAS - RETORNO	GRELHA DE ALETAS FIXAS COM REGISTRO	3 Unidades
		Marca de referência: Trox; Modelo: VAT-AG; 325x125 mm	
GE-01	GRELHA DE ALETAS FIXAS - EXAUSTÃO	GRELHA DE ALETAS FIXAS COM REGISTRO	8 Unidades
		Marca de referência: Trox; Modelo: VAT-AG; 225 x 125 mm	
GE-02	GRELHA DE ALETAS FIXAS - EXAUSTÃO	GRELHA DE ALETAS FIXAS COM REGISTRO	3 Unidades
		Marca de referência: Trox; Modelo: VAT-AG; 325 x 125 mm	
GE-03	GRELHA DE ALETAS FIXAS - EXAUSTÃO	GRELHA DE ALETAS FIXAS COM REGISTRO	1 Unidades
		Marca de referência: Trox; Modelo: VAT-AG; 625 x 125 mm	

DUTOS FLEXÍVEIS - NOVOS

TAG	DESCRIÇÃO	ESPECIFICAÇÃO	QUANTIDADE
DF-01	DUTO FLEXÍVEL	DUTO FLEXÍVEL ISOLADO Ø12cm	12 m
		Referência: Multivac - Isodec	
DF-02	DUTO FLEXÍVEL	DUTO FLEXÍVEL ISOLADO Ø30,5cm	6 m
		Referência: Multivac - Isodec	
DF-03	DUTO FLEXÍVEL	DUTO FLEXÍVEL ISOLADO Ø20,3cm	12 m
		Referência: Multivac - Isodec	

REVISÃO	DESCRIÇÃO	DATA
00	EMISSÃO INICIAL	21/11/2023

CLIENTE(S)

Brazil Hospitality Group

PROJETISTA

OBRA: ACADEMIA - HOTEL GRAND MERCURE - RIO DE JANEIRO - RJ

DISCIPLINA: HVAC

ETAPA: PROJETO EXECUTIVO

PRANCHA: 001/03

DESENHO: PLANTA DE AR CONDICIONADO - 18º PAV.

REVISÃO: 00

LOCAL: Avenida Atlântica,3716 Rio de Janeiro/RJ

RESPONSÁVEL TÉCNICO: VINICIUS MAIA DA SILVA CREA: 2011119632

ESCALA: INDICADA

ARQUIVO DIGITAL: 001-HGM-VAC-PE-PB-R00.DWG

EQUIPE TÉCNICA: PEDRO AUGUSTO GOMES ALVES SILVA

DATA: 21/11/2023