CONDICIONADORES DE AR - NOVOS

	TAG	AC-01/02/03	AC-04	AC-05/06/07	AC-08 AO AC-15 E AC-31	AC-16 AO AC-22	AC-23 E AC-24	AC-25 AO AC-30
	QUANTIDADE	03	01	03	09	07	02	06
	FABRICANTE	CARRIER	CARRIER	CARRIER	CARRIER	CARRIER	CARRIER	CARRIER
	CAPACIDADE (BTU/h / TR)	57.000 / 4,75	22.000 / 1.83	12.000 / 1,00	9.000 / 0,75	46.000 / 3,42	22.000 / 1.83	36.000 / 3
	FLUÍDO REFRIGERANTE	R-410A	R-410A	R-410A	R-410A	R-410A	R-410A	R-410A
EVAPORADOR	TIPO	TETO	HIGH WALL	HIWALL	HIWALL	CASSETE	HIGH WALL	CASSETE
	MODELO	42ZQA60C5	42MACA22S5	42FVCA12C5	42FVCA09C5	40KWQU48C5	42MACA22S5	40KWQU36C5
	TIPO VENTILADOR	CENTRÍFUGO	CENTRÍFUGO	CENTRÍFUGO	CENTRÍFUGO	CENTRÍFUGO	CENTRÍFUGO	CENTRÍFUGO
	VAZÃO AR (m3/h)	2380	1.200	600	480	2.000	1.200	1.800
	PRESSÃO ESTÁTICA TOTAL (mmca)	-	-	-	-	-	-	-
	CLASSE DE FILTRO	G3	G3	G3	G3	G3	G3	G3
	PESO EVAP. (kg)	45,8	12,5	7,8	8,0	28,1	12,5	24,5
CONDENSADORA	TAG	UC-01/02/03	UC-22 E UC-23	UC-05/06/07	UC-08 AO UC-15 E UC-31	UC-16 AO UC-21	UC-22 E UC-23	UC-25 AO UC-30
	MODELO	38CQUJ060535MC	42MACA22S5	38FVCA12C5	38FVCA09C5	38CCU048535MC	42MACA22S5	38CCU036515MC
	PESO COND. (kg)	73,5	43,5	26,5	23,5	60,4	43,5	45,6
	ALIMENTAÇÃO	220V/3F/60 Hz	220V/1F/60 Hz	220V/1F/60 Hz	220V/1F/60 Hz	220V/1F/60 Hz	220V/1F/60 Hz	220V/1F/60 Hz
	POT. (kW)	5,5 kW	1,9 kW	1,1 kW	0,8 kW	4,45 kW	1,9 kW	3,5 kW
	OBSERVAÇÃO	FRIO	FRIO	FRIO	FRIO	FRIO	FRIO	FRIO

CONDICIONADORES DE AR - REMANEJADOS*

	TAG	CA-15 AO CA-17
	QUANTIDADE	03
	FABRICANTE	SPRINGER MIDEA
	CAPACIDADE (BTU/h / TR)	36.000 / 3.00
	FLUÍDO REFRIGERANTE	R-410A
EVAPORADOR	TIPO	PISO TETO
	MODELO	42XQO36S5
	TIPO VENTILADOR	CENTRÍFUGO
	VAZÃO AR (m3/h)	1500
	PRESSÃO ESTÁTICA TOTAL (mmca)	-
	CLASSE DE FILTRO	G3
	PESO EVAP. (kg)	27,2
CONDENSADORA	TAG	CON-15 AO CON-17
	MODELO	42XQO36S5
	PESO COND. (kg)	50,0
	ALIMENTAÇÃO	220V/1F/60 Hz
	POT. (kW)	3,800 kW
	OBSERVAÇÃO	FRIO

CONDICIONADORES DE AR - MANTER*

	TAG	CA-21 E CA-23	CA-13 E CA-14	CA-27 E CA-28
	QUANTIDADE	03	02	02
	FABRICANTE	SPRINGER MIDEA	CARRIER	CARRIER
	CAPACIDADE (BTU/h / TR)	9.000 / 0.75	48.000 / 4.00	22.000 / 1.83
	FLUÍDO REFRIGERANTE	R-410A	R-410A	R-410A
EVAPORADOR	TIPO	HIGH WALL	CASSETE	HIGH WALL
	MODELO	42MACB09S5	40KWCD48C5	42MACA22S5
	TIPO VENTILADOR	CENTRÍFUGO	CENTRÍFUGO	CENTRÍFUGO
	VAZÃO AR (m3/h)	497	2000	1.200
	PRESSÃO ESTÁTICA TOTAL (mmca)	-	-	-
	CLASSE DE FILTRO	G3	G3	G3
	PESO EVAP. (kg)	6,8	34,4	12,5
CONDENSADORA	TAG	CON-22 E CON-23	CON-13 E CON-14	CON-13 E CON-14
	MODELO	42MACB09S5	40KWCD48C5	42MACA22S5
	PESO COND. (kg)	23,0	104,0	43,5
	ALIMENTAÇÃO	220V/1F/60 Hz	220V/1F/60 Hz	220V/1F/60 Hz
	POT. (kW)	0,850 kW	3,800 kW	1,9 kW
	OBSERVAÇÃO	FRIO	FRIO	FRIO

* NOTA - TAGS DOS EQUIPAMENTOS EXISTENTES MANTIDAS COM A REFERÊNCIA DO AS BUILT
AC_AGCO_MEZANINO_AS BUILT_R01 E AC_AGCO_TÉRREO_AS BUILT_R01

CONDICIONADORES DE AR - REMOVIDOS*

	TAG	CA-18 AO CA-20
	QUANTIDADE	03
	FABRICANTE	SPRINGER MIDEA
	CAPACIDADE (BTU/h / TR)	36.000 / 3.00
	FLUÍDO REFRIGERANTE	R-410A
EVAPORADOR	TIPO	PISO TETO
	MODELO	42XQO36S5
	TIPO VENTILADOR	CENTRÍFUGO
	VAZÃO AR (m3/h)	1500
	PRESSÃO ESTÁTICA TOTAL (mmca)	-
	CLASSE DE FILTRO	G3
	PESO EVAP. (kg)	27,2
CONDENSADORA	TAG	CON-20
	MODELO	42XQO36S5
	PESO COND. (kg)	50,0
	ALIMENTAÇÃO	220V/1F/60 Hz
	POT. (kW)	3,800 kW
	OBSERVAÇÃO	FRIO

LISTA DE ÍTENS - NOVOS

ITEM	DESCRIÇÃO	DISCRIMINAÇÃO	QTD
GI-01	GRELHA DE ALETAS AJUSTÁVEIS - AR EXTERIOR	GRELHA DE ALETAS AJUSTÁVEIS COM REGISTRO REF. TROX - MOD. VAT-AG - TAM. 325X125mm	27
GI-02	GRELHA DE ALETAS AJUSTÁVEIS - AR EXTERIOR	GRELHA DE ALETAS AJUSTÁVEIS COM REGISTRO REF. TROX - MOD. VAT-AG - TAM. 525X225mm	11
GI-03	GRELHA DE ALETAS AJUSTÁVEIS - AR EXTERIOR	GRELHA DE ALETAS AJUSTÁVEIS COM REGISTRO REF. TROX - MOD. VAT-AG - TAM. 1225X225mm	01
GE-01	GRELHA DE ALETAS FIXAS - EXAUSTÃO	GRELHA DE ALETAS FIXAS COM REGISTRO REF. TROX - MOD. AR-AG - TAM. 225X125mm	12
GE-02	GRELHA DE ALETAS FIXAS - EXAUSTÃO	GRELHA DE ALETAS FIXAS COM REGISTRO REF. TROX - MOD. AR-AG - TAM. 325X225mm	10
DR-01	DAMPER DE LAMINAS OPOSTAS COM REGULAGEM MANUAL	DAMPER DE REGULAGEM MANUAL REF. TROX - MOD. RL-B - TAMANHO: 15X15 cm	13
DR-02	DAMPER DE LAMINAS OPOSTAS COM REGULAGEM MANUAL	DAMPER DE REGULAGEM MANUAL REF. TROX - MOD. RL-B - TAMANHO: 25X20 cm	04
DR-03	DAMPER DE LAMINAS OPOSTAS COM REGULAGEM MANUAL	DAMPER DE REGULAGEM MANUAL REF. TROX - MOD. RL-B - TAMANHO: 40X25 cm	01
DR-04	DAMPER DE LAMINAS OPOSTAS COM REGULAGEM MANUAL	DAMPER DE REGULAGEM MANUAL REF. TROX - MOD. RL-B - TAMANHO: 25X25 cm	04
VZ-01	VENEZIANA PARA TOMADA/DESCARGA DE AR	VENEZIANA PARA DESCARGA DE AR COM TELA REF. TROPICAL- MOD. TAE - TAM. 550X300mm	01
GP-01	GRELHA DE PORTA	GRELHA DE PORTA COM DUPLA MOLDURA REF. TROX- MOD. AGS-T - TAM. 425X225mm	02
GP-01	GRELHA DE PORTA	GRELHA DE PORTA COM DUPLA MOLDURA REF. TROX- MOD. AGS-T - TAM. 325X125mm	01
DS-01	DAMPER DE SOBREPRESSÃO	DAMPER DE SOBREPRESSÃO REF. TROX - MOD. KUL - TAMANHO: 55X25 cm	02

VENTILADORES - NOVOS

	TAG	CV-01/02/04/05/06	CV-03	EX-01 AO EX-03	EX-05 AO EX-06
	QUANTIDADE	05	01	03	02
	FABRICANTE	BERLINER LUFT	BERLINER LUFT	SOLER&PALAU	SICFLUX
	MODELO	BBT 160	BBT 355	VENT-315B	FH-315
	FILTRO	M5	M5	-	-
VENTILADOR	VAZÃO AR (m3/h)	(PROJETO)	4.725	(PROJETO)	1.840
	PRESSÃO ESTÁTICA DISPONÍVEL (mmca)	20-25	30	20	25
	TIPO VENTILADOR	CENTRÍFUGO	CENTRÍFUGO	AXIAL	CENTRÍFUGO
	ROTAÇÃO (RPM)	-	849	2730	-
	PESO (kg)	-	155	8	28
	ARRANJO	-	-	-	-
	ALIMENTAÇÃO	220 V / 3F / 60 Hz	220 V / 3F / 60 Hz	220 V / 1F / 60 Hz	220 V / 1F / 60 Hz
	POT. (kW)	0,550	0,750	0,27	0,182
	OBSERVAÇÃO	PROGRAMADOR HORÁRIO	PROGRAMADOR HORÁRIO	PROGRAMADOR HORÁRIO	PROGRAMADOR HORÁRIO

LEGENDA DE REPRESENTAÇÃO GRÁFICA - HVAC

- PONTO DE DRENO
- PONTO DE FORÇA
- QUADRO ELETRICO DOS EQUIPAMENTOS
- PONTO DE ÁGUA PARA MANUTENÇÃO DO EQUIPAMENTO
- TUBULAÇÃO FRIGORÍGENA
- DUTO DE EXAUSTÃO EM CHAPA DE AÇO GALVANIZADO SEM ISOLAMENTO TÉRMICO.
- DUTO DE AR EXTERNO EM CHAPA DE AÇO GALVANIZADO SEM ISOLAMENTO TÉRMICO.
- INSTALAÇÃO EXISTENTE A MANTER
- INSTALAÇÃO REMANEJADA
- EQUIPAMENTOS NOVOS A INSTALAR
- SENTIDO DE FLUXO DO AR DE EXTAUSTÃO
- SENTIDO DE FLUXO DO AR DE INSUFLAMENTO
- (I) INSUFLAMENTO
- (R) RETORNO
- (EX) EXAUSTÃO
- (AE) AR EXTERIOR
- (GI) GRELHA DE ISUFLAMENTO
- (GE) GRELHA DE EXAUSTÃO
- (DR) DAMPER DE REGULAGEM
- (VZ) VENEZIANA

NOTAS GERAIS

1. CONSULTAR OS DESENHOS DE DETALHES TÍPICOS, PARA COTAÇÃO E EXECUÇÃO DA OBRA PARA DEFINIÇÃO COMPLETA DO ESCOPO DE SERVIÇOS DO INSTALADOR DEVERÁ AINDA CHECAR OS ESPAÇOS PREVISTOS, COM INTUITO DE PROPOR EQUIPAMENTOS E/OU MATERIAIS COM DIMENSÕES FÍSICAS COMPATÍVEIS COM OS RESPECTIVOS LOCAIS PREVISTOS PARA INSTALAÇÃO DOS MESMOS;
2. ANTES DO INÍCIO DA OBRA, A EMPRESA RESPONSÁVEL PELA EXECUÇÃO DEVERÁ REALIZAR UM LEVANTAMENTO NO LOCAL, VERIFICANDO AS INFORMAÇÕES APRESENTADAS NO PROJETO E INTERFERÊNCIAS NA OBRA. QUALQUER ALTERAÇÃO QUE SE FAÇA NECESSARIO NA EXECUÇÃO DA OBRA A GERENCIADORA DEVERÁ SER COMUNICADA ANTES DA EXECUÇÃO DO SERVIÇOS, E A INSTALADORA DEVERÁ ENTREGAR AS-BUILT NO TERMINO DA OBRA;
3. DIMENSÕES EM CENTIMETRO, EXCETO QUANDO INDICADO DE OUTRA FORMA;
4. TODOS OS FUROS PARA PASSAGEM DE DUTOS, TUBULAÇÕES E/OU ELETRODUTOS, DEVERÃO SER VEDADOS APÓS A INSTALAÇÃO DOS MESMOS;
5. CONFERIR MEDIDAS NO LOCAL;
6. PROJETO DESENVOLVIDO SEGUNDO ORIENTAÇÕES DA ABNT 16401-1/3 E ANVISA REn°9;
7. EFETUAR AS DEVIDAS ADEQUAÇÕES E RECOPOSIÇÕES DE ALVENARIA/FORRO; (FUROS, CONSTRUÇÃO DE PAREDES, ETC.);
8. O INSTALADOR DEVERÁ FORNECER LAUDO DE TESTES, GARANTIA DOS EQUIPAMENTOS E DA OBRA E ART NA CONCLUSÃO DA OBRA;
9. O INSTALADOR DEVERÁ VERIFICAR A TENSÃO ELÉTRICA DO LOCAL ANTES DA COMPRA DOS EQUIPAMENTOS DE FORMA FORNECER O EQUIPAMENTO CONFORME A TENSÃO DE OPERAÇÃO DO LOCAL;
10. CONSULTAR PROJETO ELÉTRICO PARA O ALIMENTADOR DOS EQUIPAMENTOS;
11. NOTAS REFERENTES AO SISTEMA SPLIT SYSTEM:
    - 11.1. AS TUBULAÇÕES DE GÁS REFRIGERANTE DEVERÃO SER DIMENSIONADAS CONFORME ESPECIFICAÇÕES DO FABRICANTE E ISOLADAS TERMICAMENTE COM ESPUMA ELASTOMÉRICA DE ESTRUTURA CELULAR FECHADA. AS LINHAS DE SUCÇÃO E LIQUIDO, DEVERÃO POSSUIR UMA ESPUMA PARA CADA, NAS DIMENSÕES CONFORME BITOLA DAS MESMAS;
    - 11.2. A DISTÂNCIA ENTRA A UNIDADE CONDENSADORA E EVAPORADORA NÃO DEVÉ ULTRAPASSAR O RECOMENDADO NO MANUAL DE INSTALAÇÃO DO EQUIPAMENTO. PARA EVENTUAL INSTALAÇÃO COM LINHA ACIMA DO PADRÃO ESPECIFICADO PELO FABRICANTE, DEVERÁ SER ADOTADO AS DIMENSÕES E INSTALAÇÃO DE ACESSÓRIOS CONFORME ESPECIFICAÇÃO DE LINHAS LONGAS DO FABRICANTE DO EQUIPAMENTO, OBEDECENDO AOS LIMITES DETERMINADOS NO MANUAL DE INSTALAÇÃO;
    - 11.3. DEVERÁ SER ANALISADO PELA INSTALADORA A MELHOR MANEIRA PARA EXECUÇÃO DAS TUBULAÇÕES. O INSTALADOR PODERÁ MODIFICAR O ENCAMINHAMENTO DA TUBULAÇÃO DE COBRE, PARA DIMINUIR SEU TRAJETO OU DESVIAR DE EVENTUAIS INTERFERÊNCIAS, DESDE QUE SEJAM RESPEITADOS OS LIMITES IMPOSTOS PELO FABRICANTE DOS EQUIPAMENTOS;
    - 11.4. A INTERLIGAÇÃO ENTRE A UNIDADE CONDENSADORA E A UNIDADE EVAPORADORA DEVERÁ SER REALIZADA ATRAVÉS DE CABO PP, PELO MESMO TRAJETO DAS TUBULAÇÕES QUE INTERLIGAM A UNIDADE EVAPORADORA (APLICAÇÃO PARA SISTEMA DE MINI SPLIT DE AMBIENTE);
    - 11.5. PARA LOCAIS DE EXPOSIÇÃO A INTEMPÉRIES, PREVER PROTEÇÃO MECÂNICA PARA AS TUBULAÇÕES DE GÁS REFRIGERANTE E INTERLIGAÇÕES ELÉTRICAS EM ARGAMASSA DE BASE ACRÍLICA. FABRICANTE DE REF.: ARMACHEK;
    - 11.6. PARA LOCAIS INTERNOS OU EMBUTIDOS EM ALVENARIA, PREVER ENVOLVIMENTO NAS TUBULAÇÕES DE GÁS REFRIGERANTE E INTERLIGAÇÕES ELÉTRICAS COM FITA PVC;
    - 11.7. PREVER INTERLIGAÇÃO ENTRE O DRENO DA UNIDADE EVAPORADORA E A REDE DE DRENAGEM A SER EXECUTADA NO LOCAL. A TUBULAÇÃO DOS DRENOS DEVERÁ SER EM DE PVC SOLDÁVEL DE NO MÍNIMO Ø20mm E ISOLADA TERMICAMENTE COM ESPUMA DE POLIETILENO EXPANDIDO. A TUBULAÇÃO DEVERÁ SER EMBUTIDA NAS PAREDES E ENCAMINHADAS PARA REDE DE PLUVIAL. PREVER SIFÃO E INCLINAÇÃO MÍNIMA DE 2% NA TUBULAÇÃO DE DRENO.
    - 11.8. OS EQUIPAMENTOS DEVERÃO POSSUIR ETIQUETA COM IDENTIFICAÇÃO, CONFORME ESPECIFICAÇÕES DO PROJETO, INCLUINDO O TAG, CAPACIDADE TÉRMICA, PRESSÃO ESTÁTICA TOTAL, CLASSE DOS FILTROS, TENSÃO DE OPERAÇÃO, CONSUMO ELÉTRICO E A DATA DE INSTALAÇÃO;
    - 11.9. AS CONDENSADORAS DEVERÃO FICAR AFASTADAS DA PAREDE NO MÍNIMO 20cm;
    - 11.10. AS UNIDADES CONDENSADORAS DEVERÃO SER INSTALADAS SOBRE CALÇOS DE NEOPRENE DE 2.5 cm DE ALTURA;
    - 11.11. O INSTALADOR DE SISTEMA DE AR CONDICIONADO DEVERÁ FORNECER E INSTALAR AS FIAÇÕES E ELETRODUTOS DOS TERMOSTATOS ATÉ AS RESPECTIVAS UNIDADES CONDICIONADORAS;

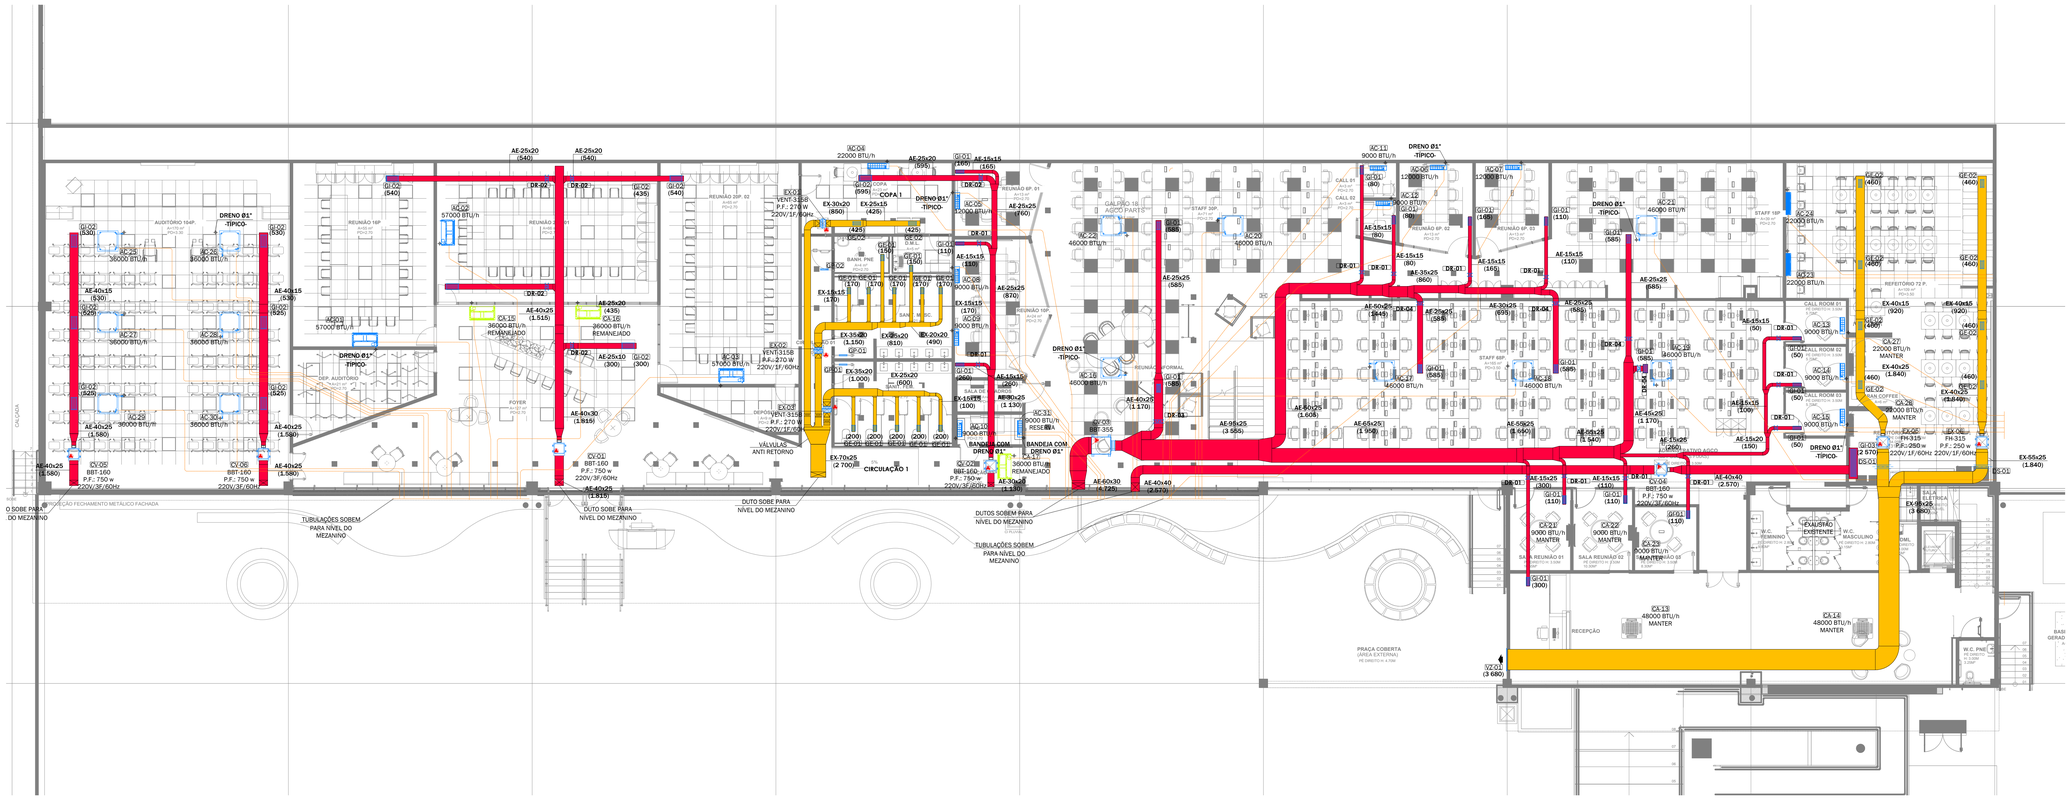

PLANTA BAIXA DE HVAC - ACADEMY - PAV. TÉRREO
ESC.: 1/100

REV.	DESCRIÇÃO	EXEC.	VERIF.	DATA
01	COMPATIBILIZAÇÃO	PA	VM	29/05/24
00	EMISSÃO INICIAL	PA	VM	19/04/24

CLIENTE: AGCO
LOCAL: Av. José Alves de Oliveira, 300 - Galpão 15, Jundiaí - SP, 13213-087
PROJETO: AGCO - INTEGRAÇÃO JUNDIAÍ X CAMPINAS
ASSUNTO: SISTEMA DE AR CONDICIONADO E VENTILAÇÃO MECÂNICA - TER- ACADEMY
FASE: PROJETO EXECUTIVO
ESPECIALIDADE: HVAC

ESCALA: 1:100 | ÁREA: 1823.00 m² | DATA: 29/05/2024
DESENHISTA: PEDRO AUGUSTO | RESP. TÉCNICO: VINICIUS MAIA 2011119632
ARQUIVO: 1850-23_P-AGCO.G18-PE-CLI-100-TER-R01.DWG

FOLHA: 100
REVISÃO: R01

akmx.com.br | 11 4000.1845
Av. Paulista, nº1499
16º andar, São Paulo-SP

TODOS OS DIREITOS RESERVADOS A AKMX ARQUITETURA E ENGENHARIA
REPRODUÇÃO E UTILIZAÇÃO SOB AUTORIZAÇÃO FORMAL DO ARQUITETO